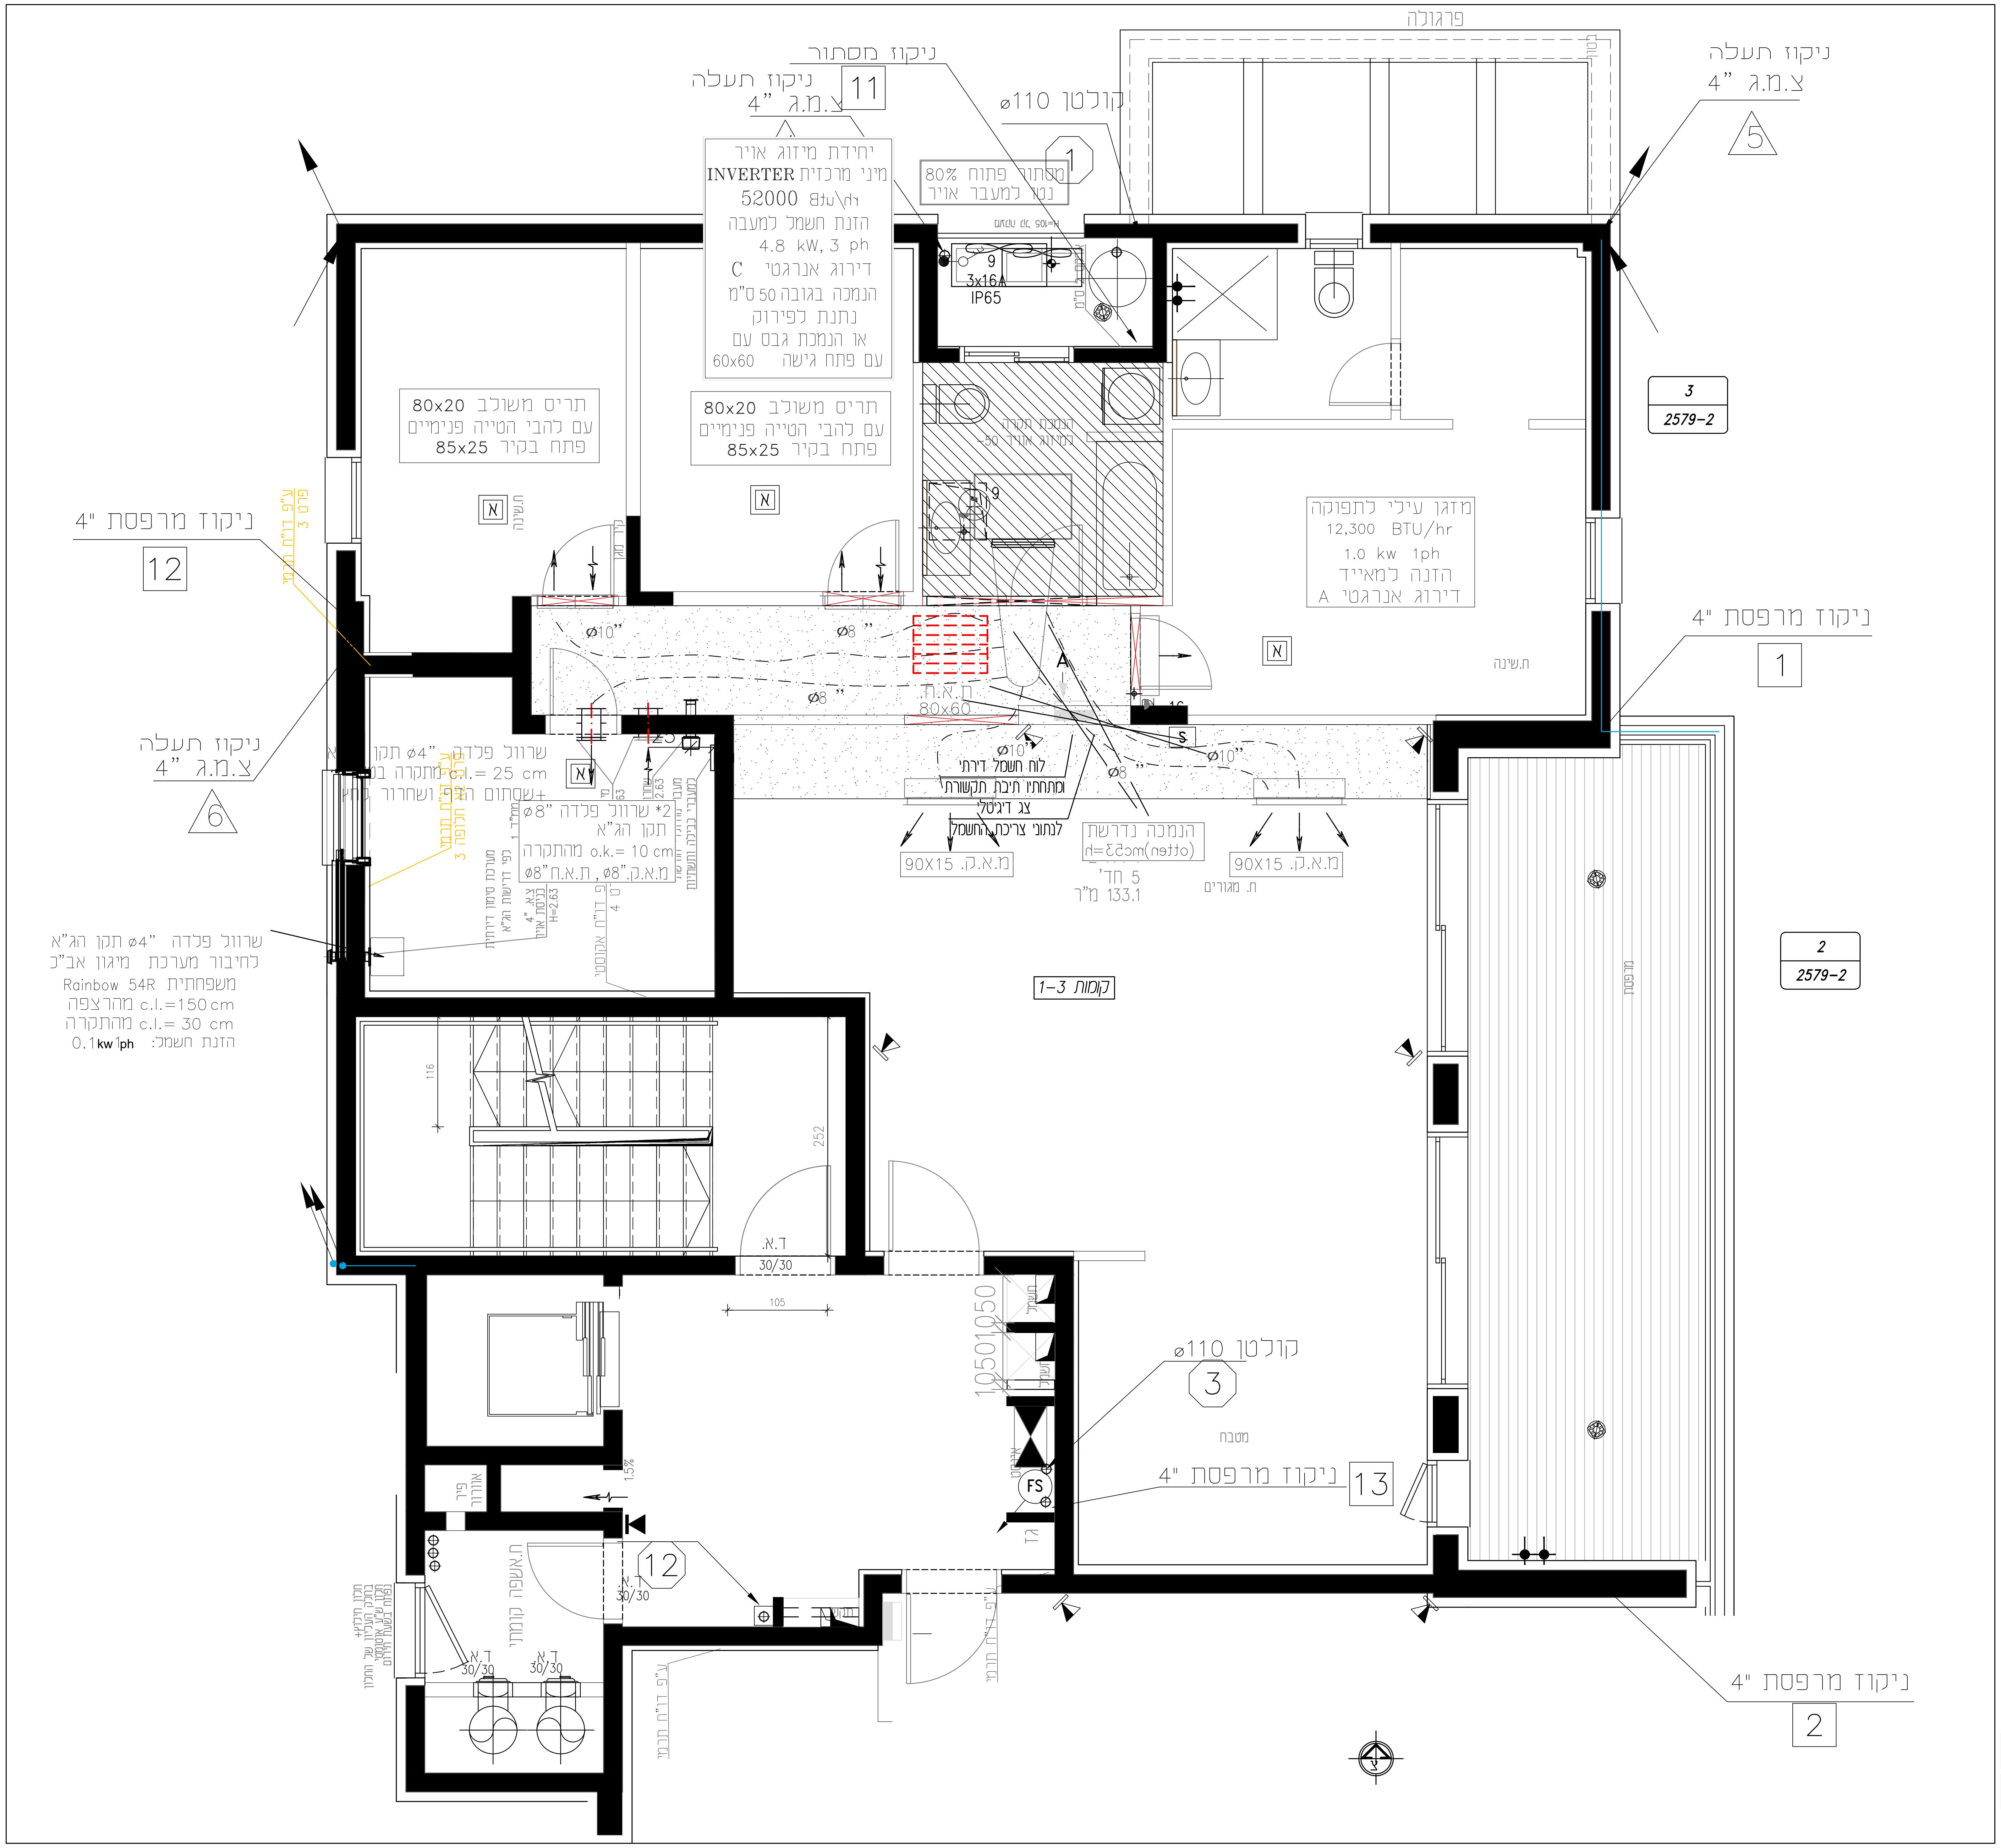

פרוייקט עלי מוהר 6-8
רעננה

תאריך: 9/2/2006

קובץ:

0

לעיון	לאישור	לביצוע
☐	☐	☒

שם התכנית:

תוכנית מיזוג אויר

קנ"מ:	גודל גליון:	מס' גליון:
1:75	A3	2

בנין A
קומה 2
דירה מס 4

תפוצה

מהדורה:	תאריך:	יזם:	קבלן:	ניהול פרויקט:	אדריכל:	קונסט':	אינסט':	חשמל:	מיזוג אויר:	מעליות:	תנועה:	בטיחות:	מגלפים:	קרקע:	אקוסטיקה:	עיצוב פנים:	מודד:	פיתוח:	שווק:	בקורת תכנון:	מודליסט:	יועץ אלומיניום:		

עדכון:

המבצע אחראי לבדיקת התכניות והתאמתן במקום. על המבצע לבקר את כל המידות, ועל כל טעות או אי התאמה, עליו להודיע למתכנן. אין לקבוע מידות ע"י מדידה בשרטוט. אין לבצע אלא עפ"י רשיון בניה תקף. מהנדס ו/או יועץ אשר שמו רשום מעל שם האדריכל בתכנית זו, נושא לבדו באחריות המקצועית והחוקית לתכנית. אין לעשות כל שימוש בתכנית זו או בדעיונות הגלומים בה, ללא אישור בכתב מאת המתכנן.

הערה: יש לבדוק ולתאם את כל מעברי המערכות בטרם ביצוע עפ"י תכניות אינסטלציה, חשמל, ומיזוג אויר.

הערות כלליות:

המבצע אחראי לבדיקת תכניות והתאמתם במקום.

על המבצע לבקר כל המידות ולהודיע למתכנן על כל טעות או אי-התאמה.

במקרה של ספק או אי התאמה יש לפנות למתכנן.

אין לקבוע מידות ע"י מדידה בשרטוטים.

אין לעשות כל שימוש בתכנית זו, או ברעיונות הגלומים בה ללא אישור בכתב מהמתכנן.

התכניות נשארות רכושו הפרטי של המתכנן.

אין המתכנן אחראי לביצוע עבודות שלא על פי תכניותיו.

מהנדס ו/או יועץ ששמו רשום מעל שם האדריכל בתכנית זו, נושא באחריות החוקית והמקצועית לתכנית.

כל התכניות בכפוף לאישור העיריה, אין לבצע עבודה עפ"י תכנית זו ללא רשיון בנייה בר-תוקף

כל התכניות בכפוף לאישור העיריה
אין לבצע עבודה עפ"י תכנית זו
ללא רשיון בניה בר-תוקף

אין לפגוע או להרוס
אלמנט קונסטרוקטיבי
כלשהו במהלך העבודה.

אישור לקוח על חלופה נבחרת	
תאריך:	חתימה
שם:	